



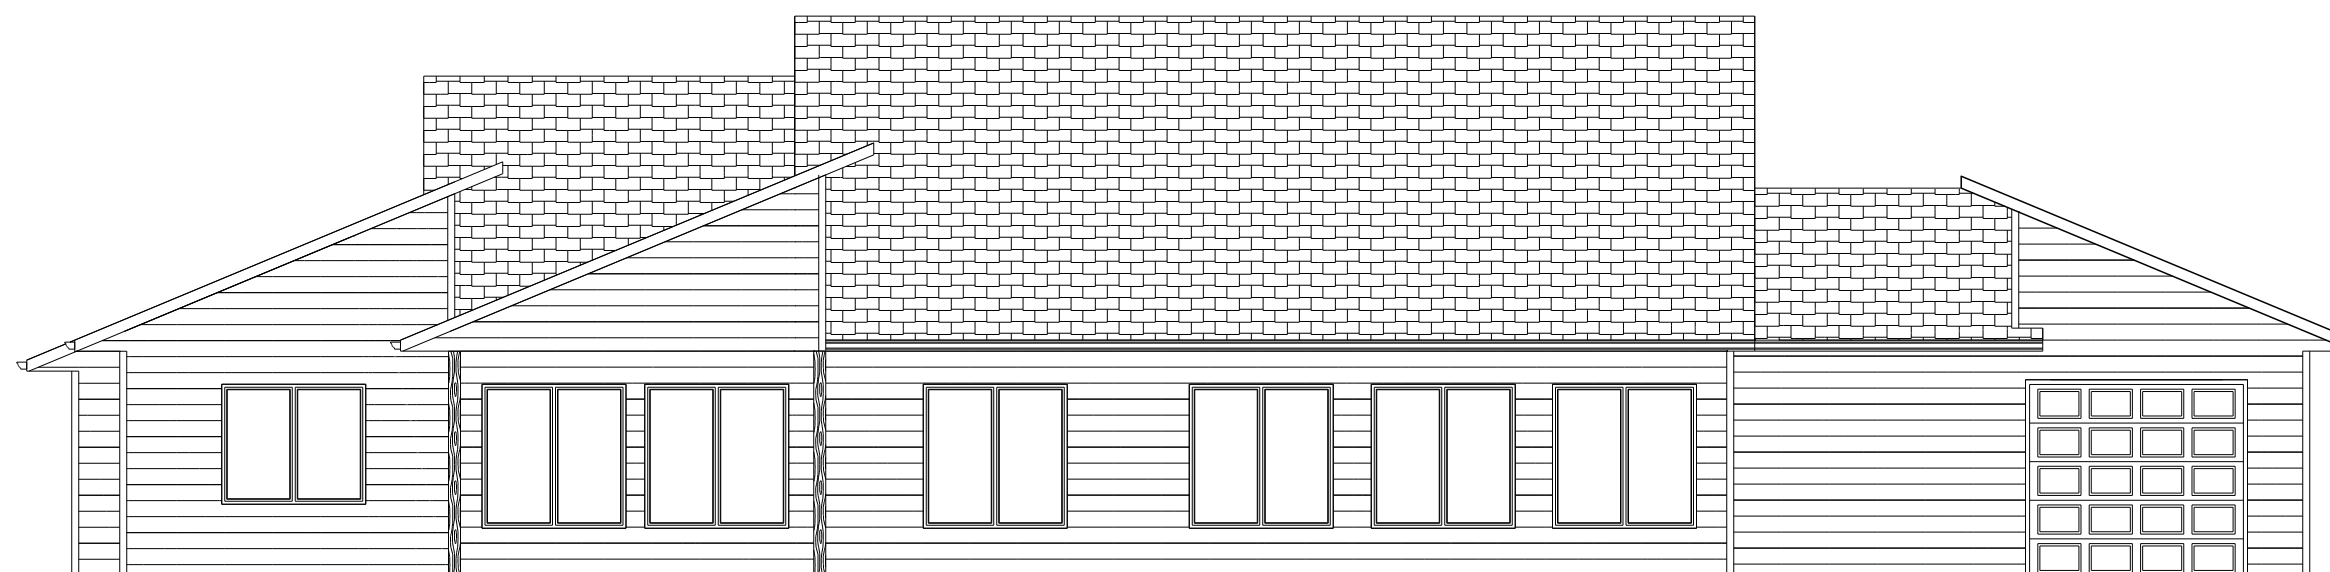


LEFT ELEVATION

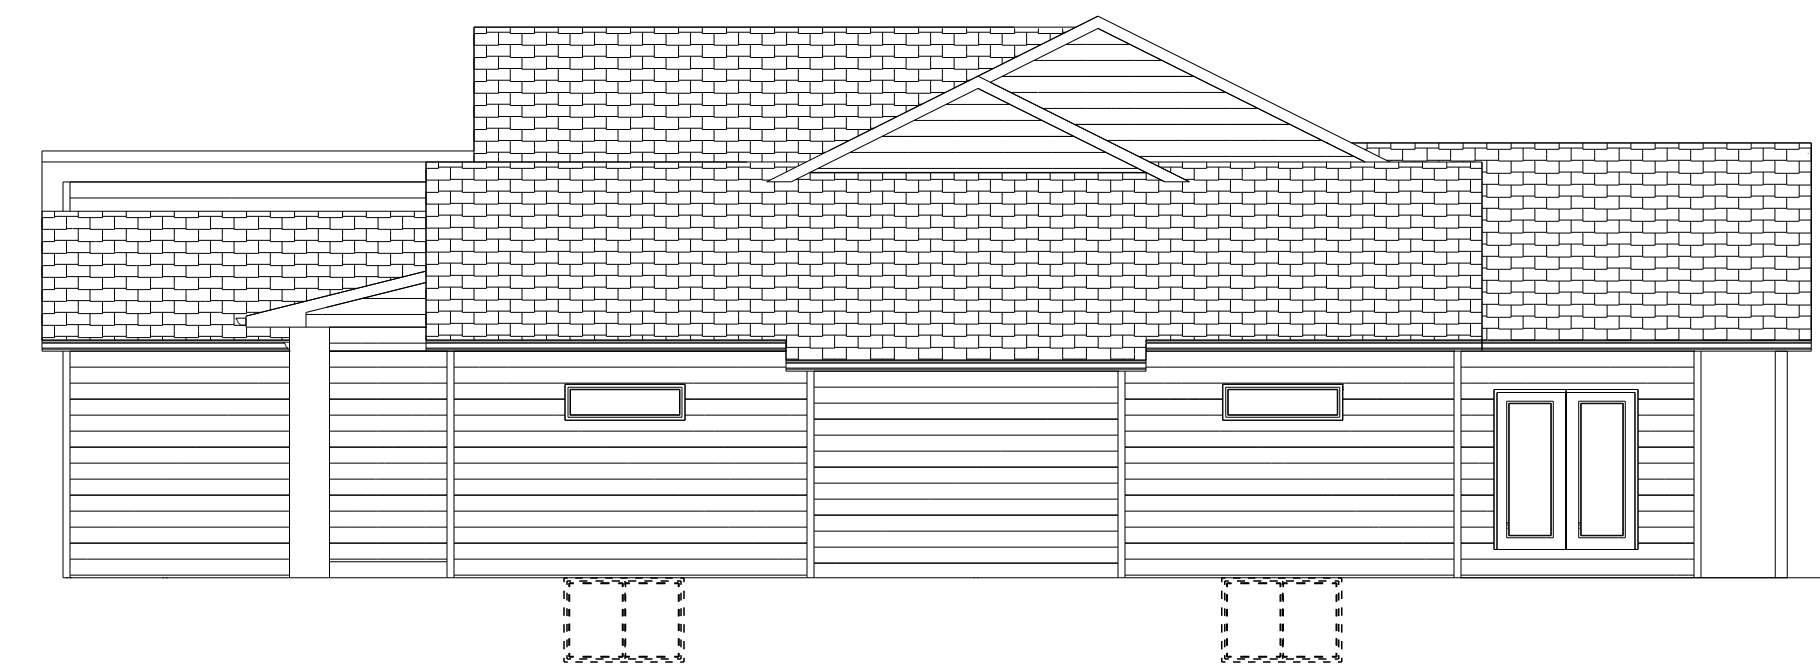

REAR ELEVATION



RIGHT ELEVATION

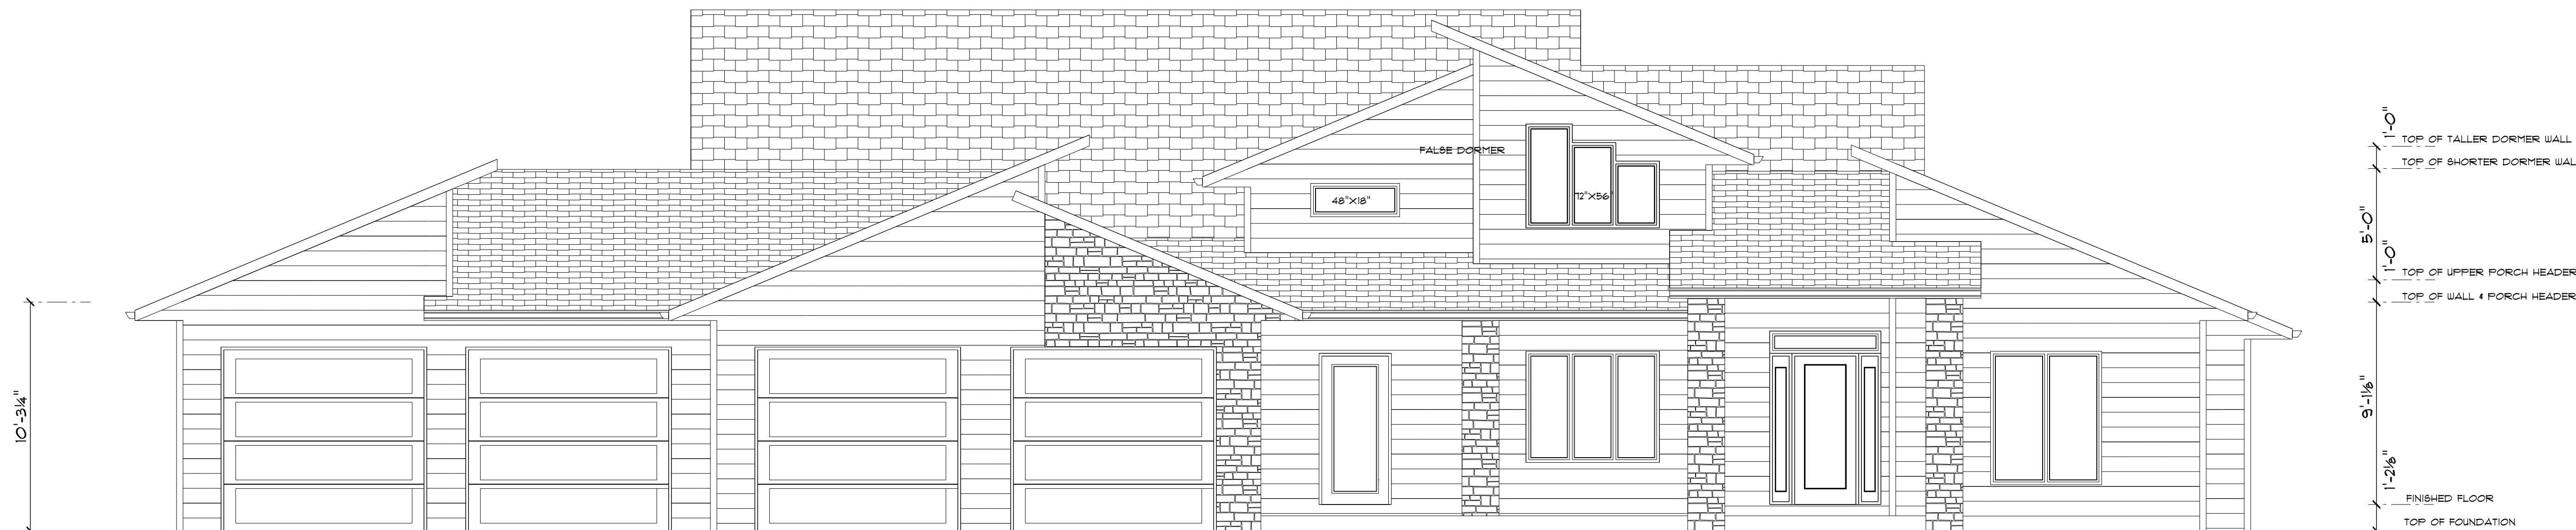

FRONT ELEVATION

1'-0" TOP OF TALLER DORMER WALL
 1'-0" TOP OF SHORTER DORMER WALL
 5'-0" TOP OF UPPER PORCH HEADER
 1'-0" TOP OF WALL & PORCH HEADER
 9'-11 1/2" FINISHED FLOOR
 1'-2 1/8" TOP OF FOUNDATION


NEW RESIDENCE FOR:
THE LAUNDRIE FAMILY

WISCONSIN

DRAWN BY: M.P.
 DATE: 9-15-2025
 SCALE: 1/4" = 1'-0"
 DRAWING NO.:

ALTHOUGH EVERY EFFORT
 HAS BEEN MADE IN
 PREPARING THESE PLANS
 AND CHECKING THEM FOR
 ACCURACY, THE
 CONTRACTOR MUST CHECK
 ALL DETAILS AND
 DIMENSIONS AND BE
 RESPONSIBLE FOR SAME.

SHEET NO.:
 1 OF 4

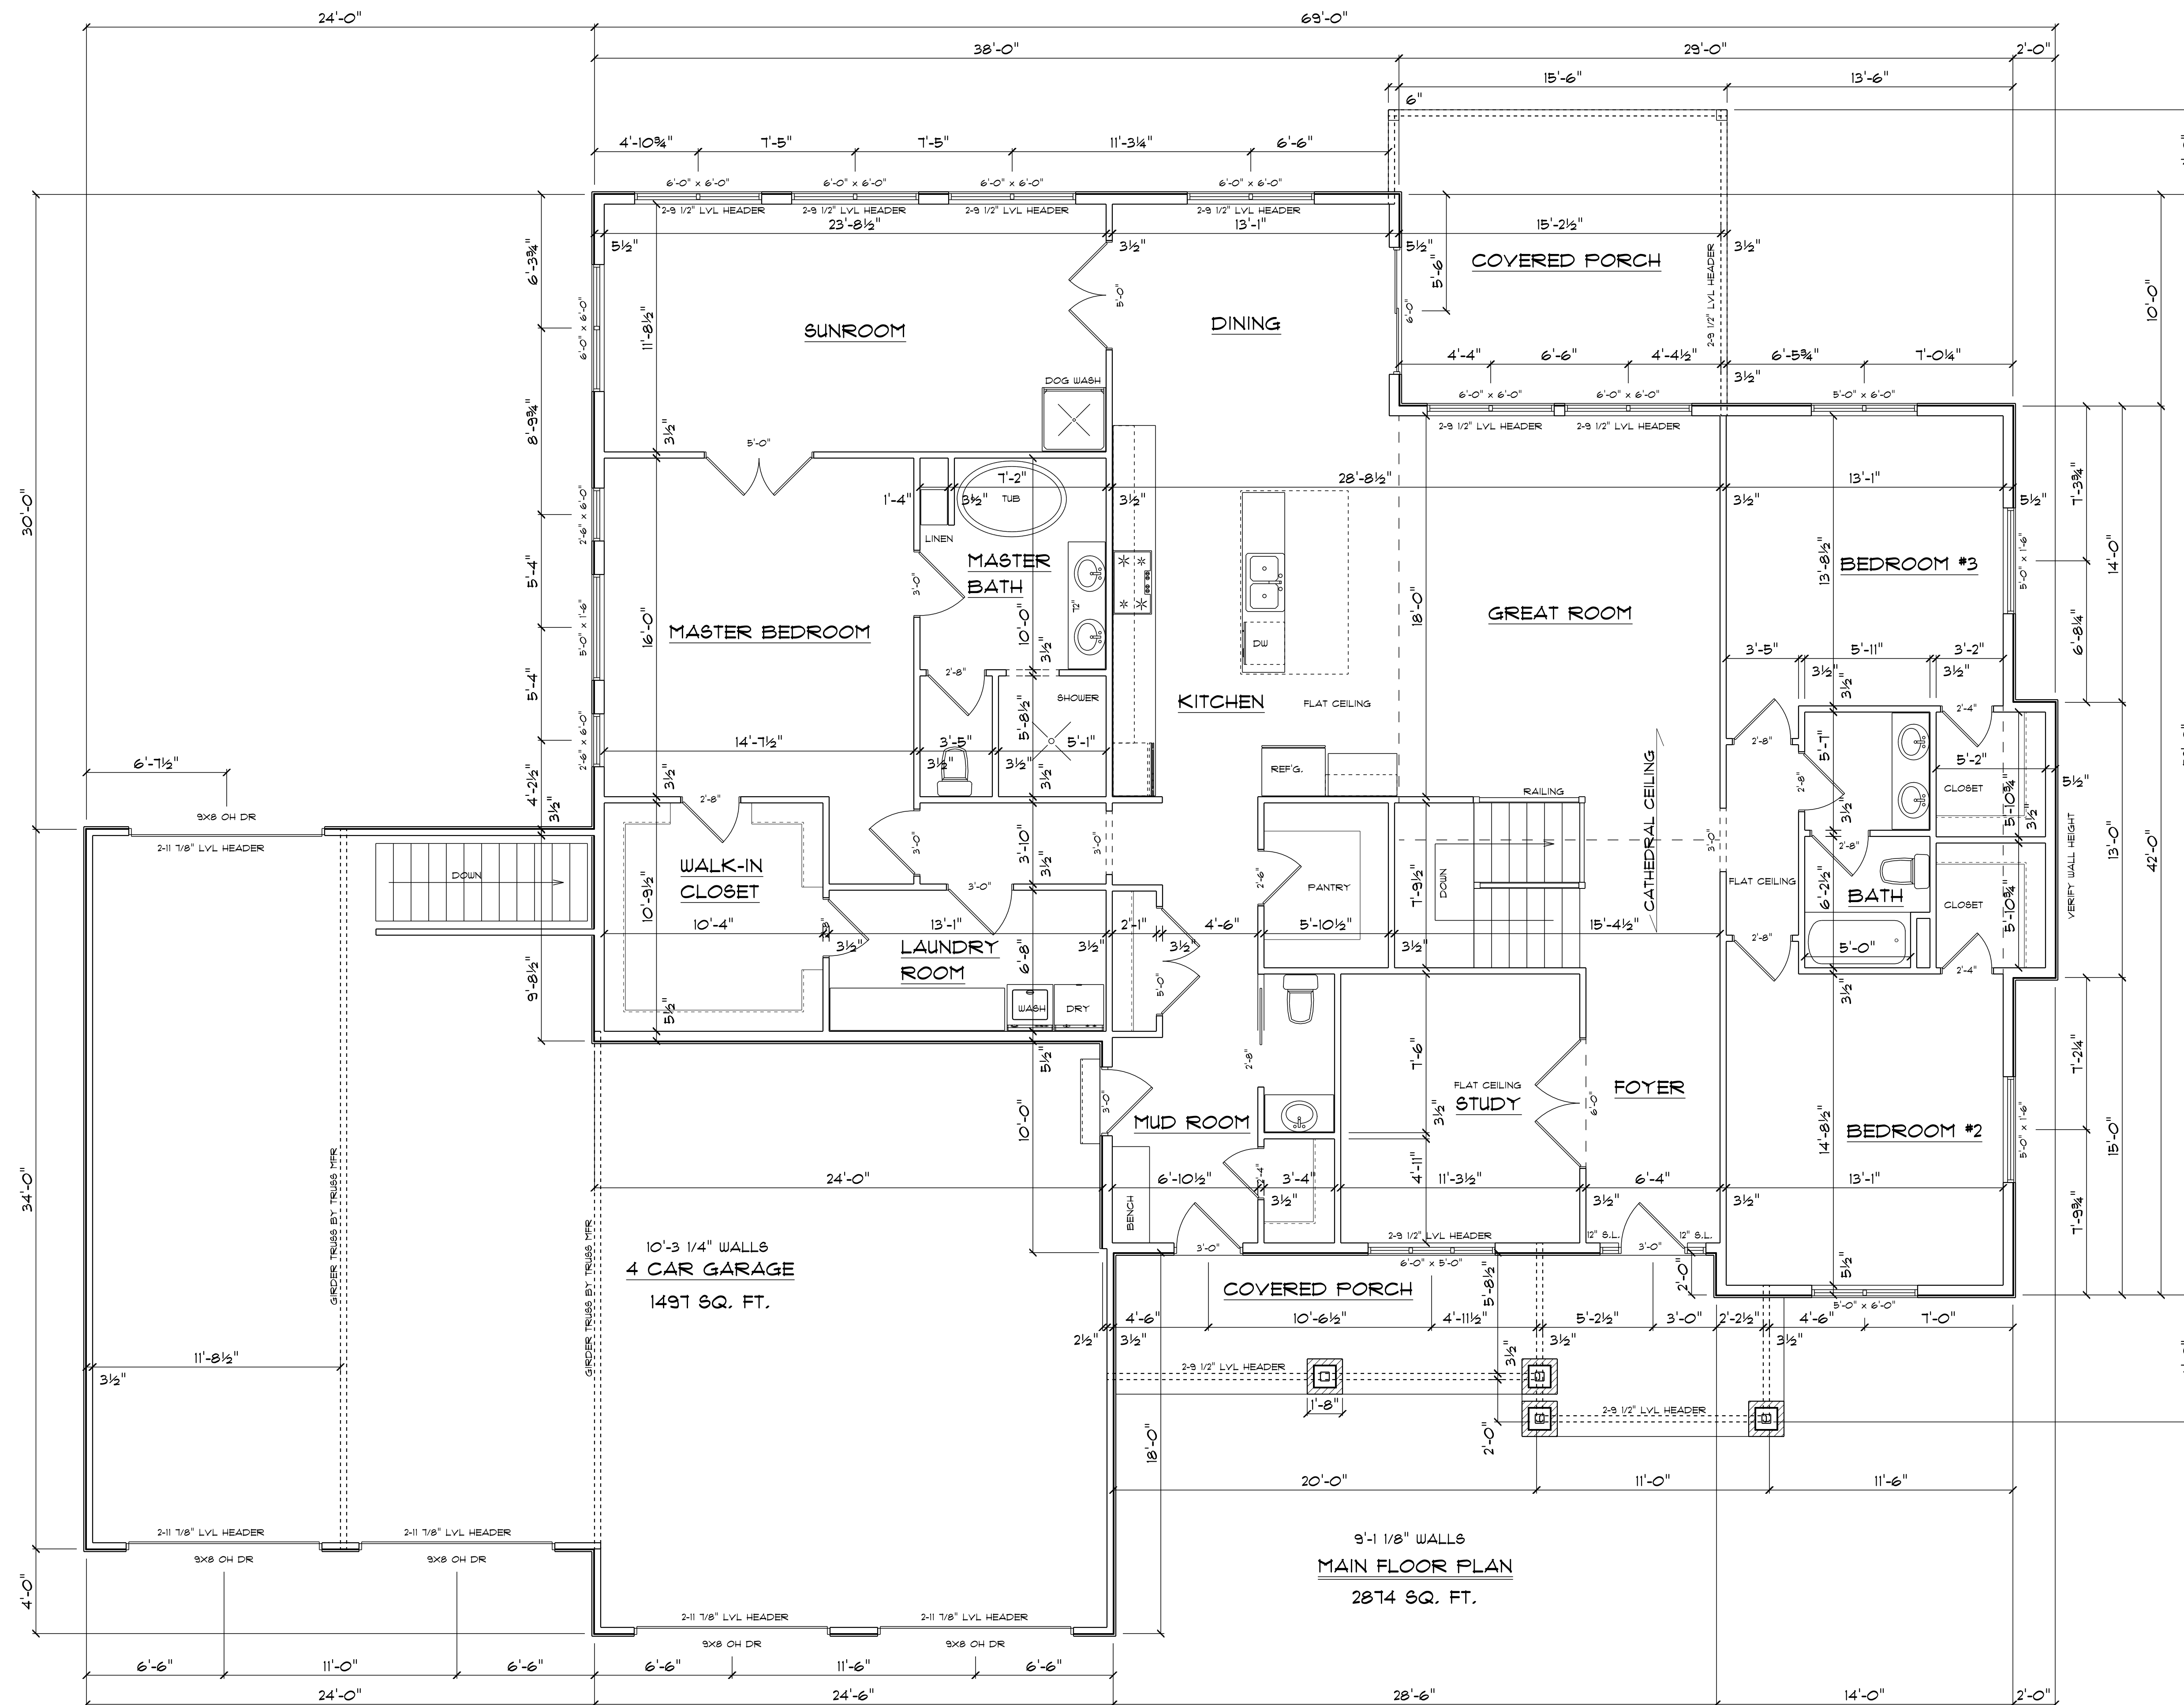

ALL HEADERS TO BE 2 FLY 2X10
#2 SPF OR BETTER UNLESS NOTED


REVISION DATE:

NEW RESIDENCE FOR:
THE LAUNDRIE FAMILY
WISCONSIN

DRAWN BY: M.P.
DATE: 9-15-2025
SCALE: 1/4"=1'-0"

DRAWING NO.:
ALTHOUGH EVERY EFFORT
HAS BEEN MADE IN
PREPARING THESE PLANS
AND CHECKING THEM FOR
ACCURACY, THE
CONTRACTOR MUST CHECK
ALL DETAILS AND
DIMENSIONS AND BE
RESPONSIBLE FOR SAME.

SHEET NO.:
2
OF
4

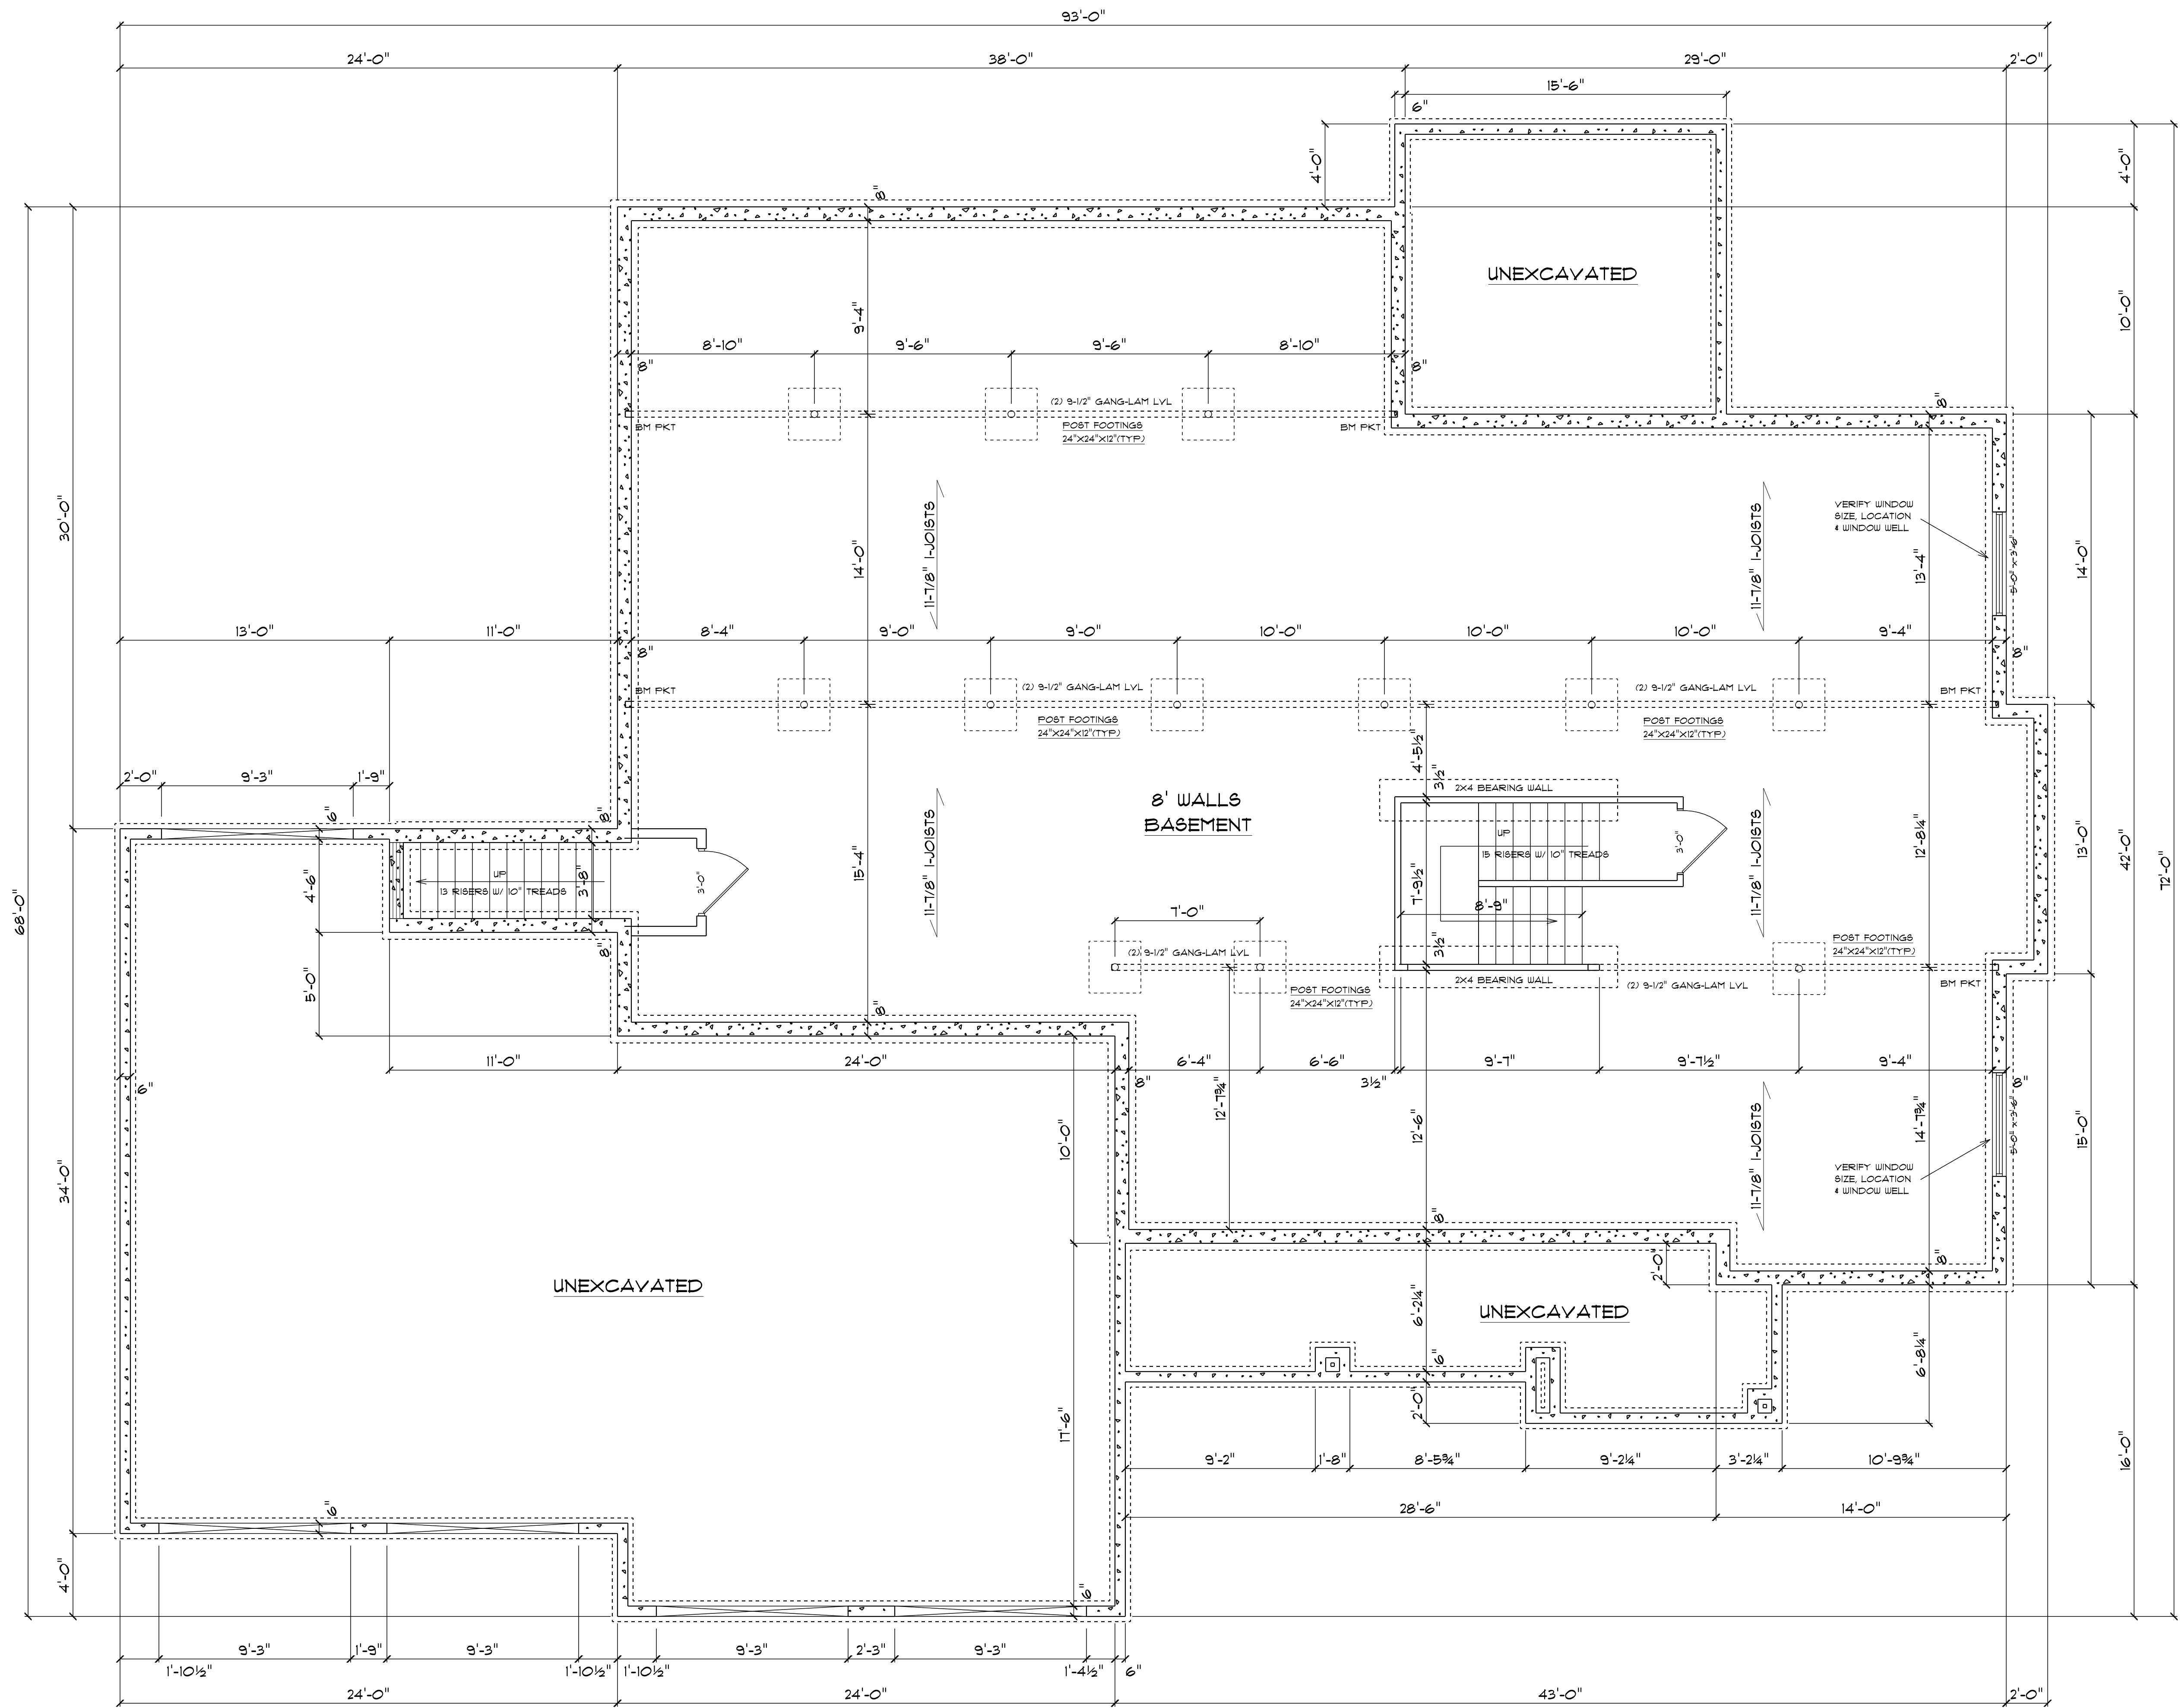

FOUNDATION PLAN

REVISION DATE:

NEW RESIDENCE FOR:
THE LAUNDRIE FAMILY

WISCONSIN

DRAWN BY: M.P.

DATE: 9-15-2025

SCALE: 1/4"=1'-0"


DRAWING NO.

ALTHOUGH EVERY EFFORT
HAS BEEN MADE IN
PREPARING THESE PLANS
AND CHECKING THEM FOR
ACCURACY, THE
CONTRACTOR MUST CHECK
ALL DETAILS AND
DIMENSIONS AND BE
RESPONSIBLE FOR SAME.

SHEET NO.

3

4

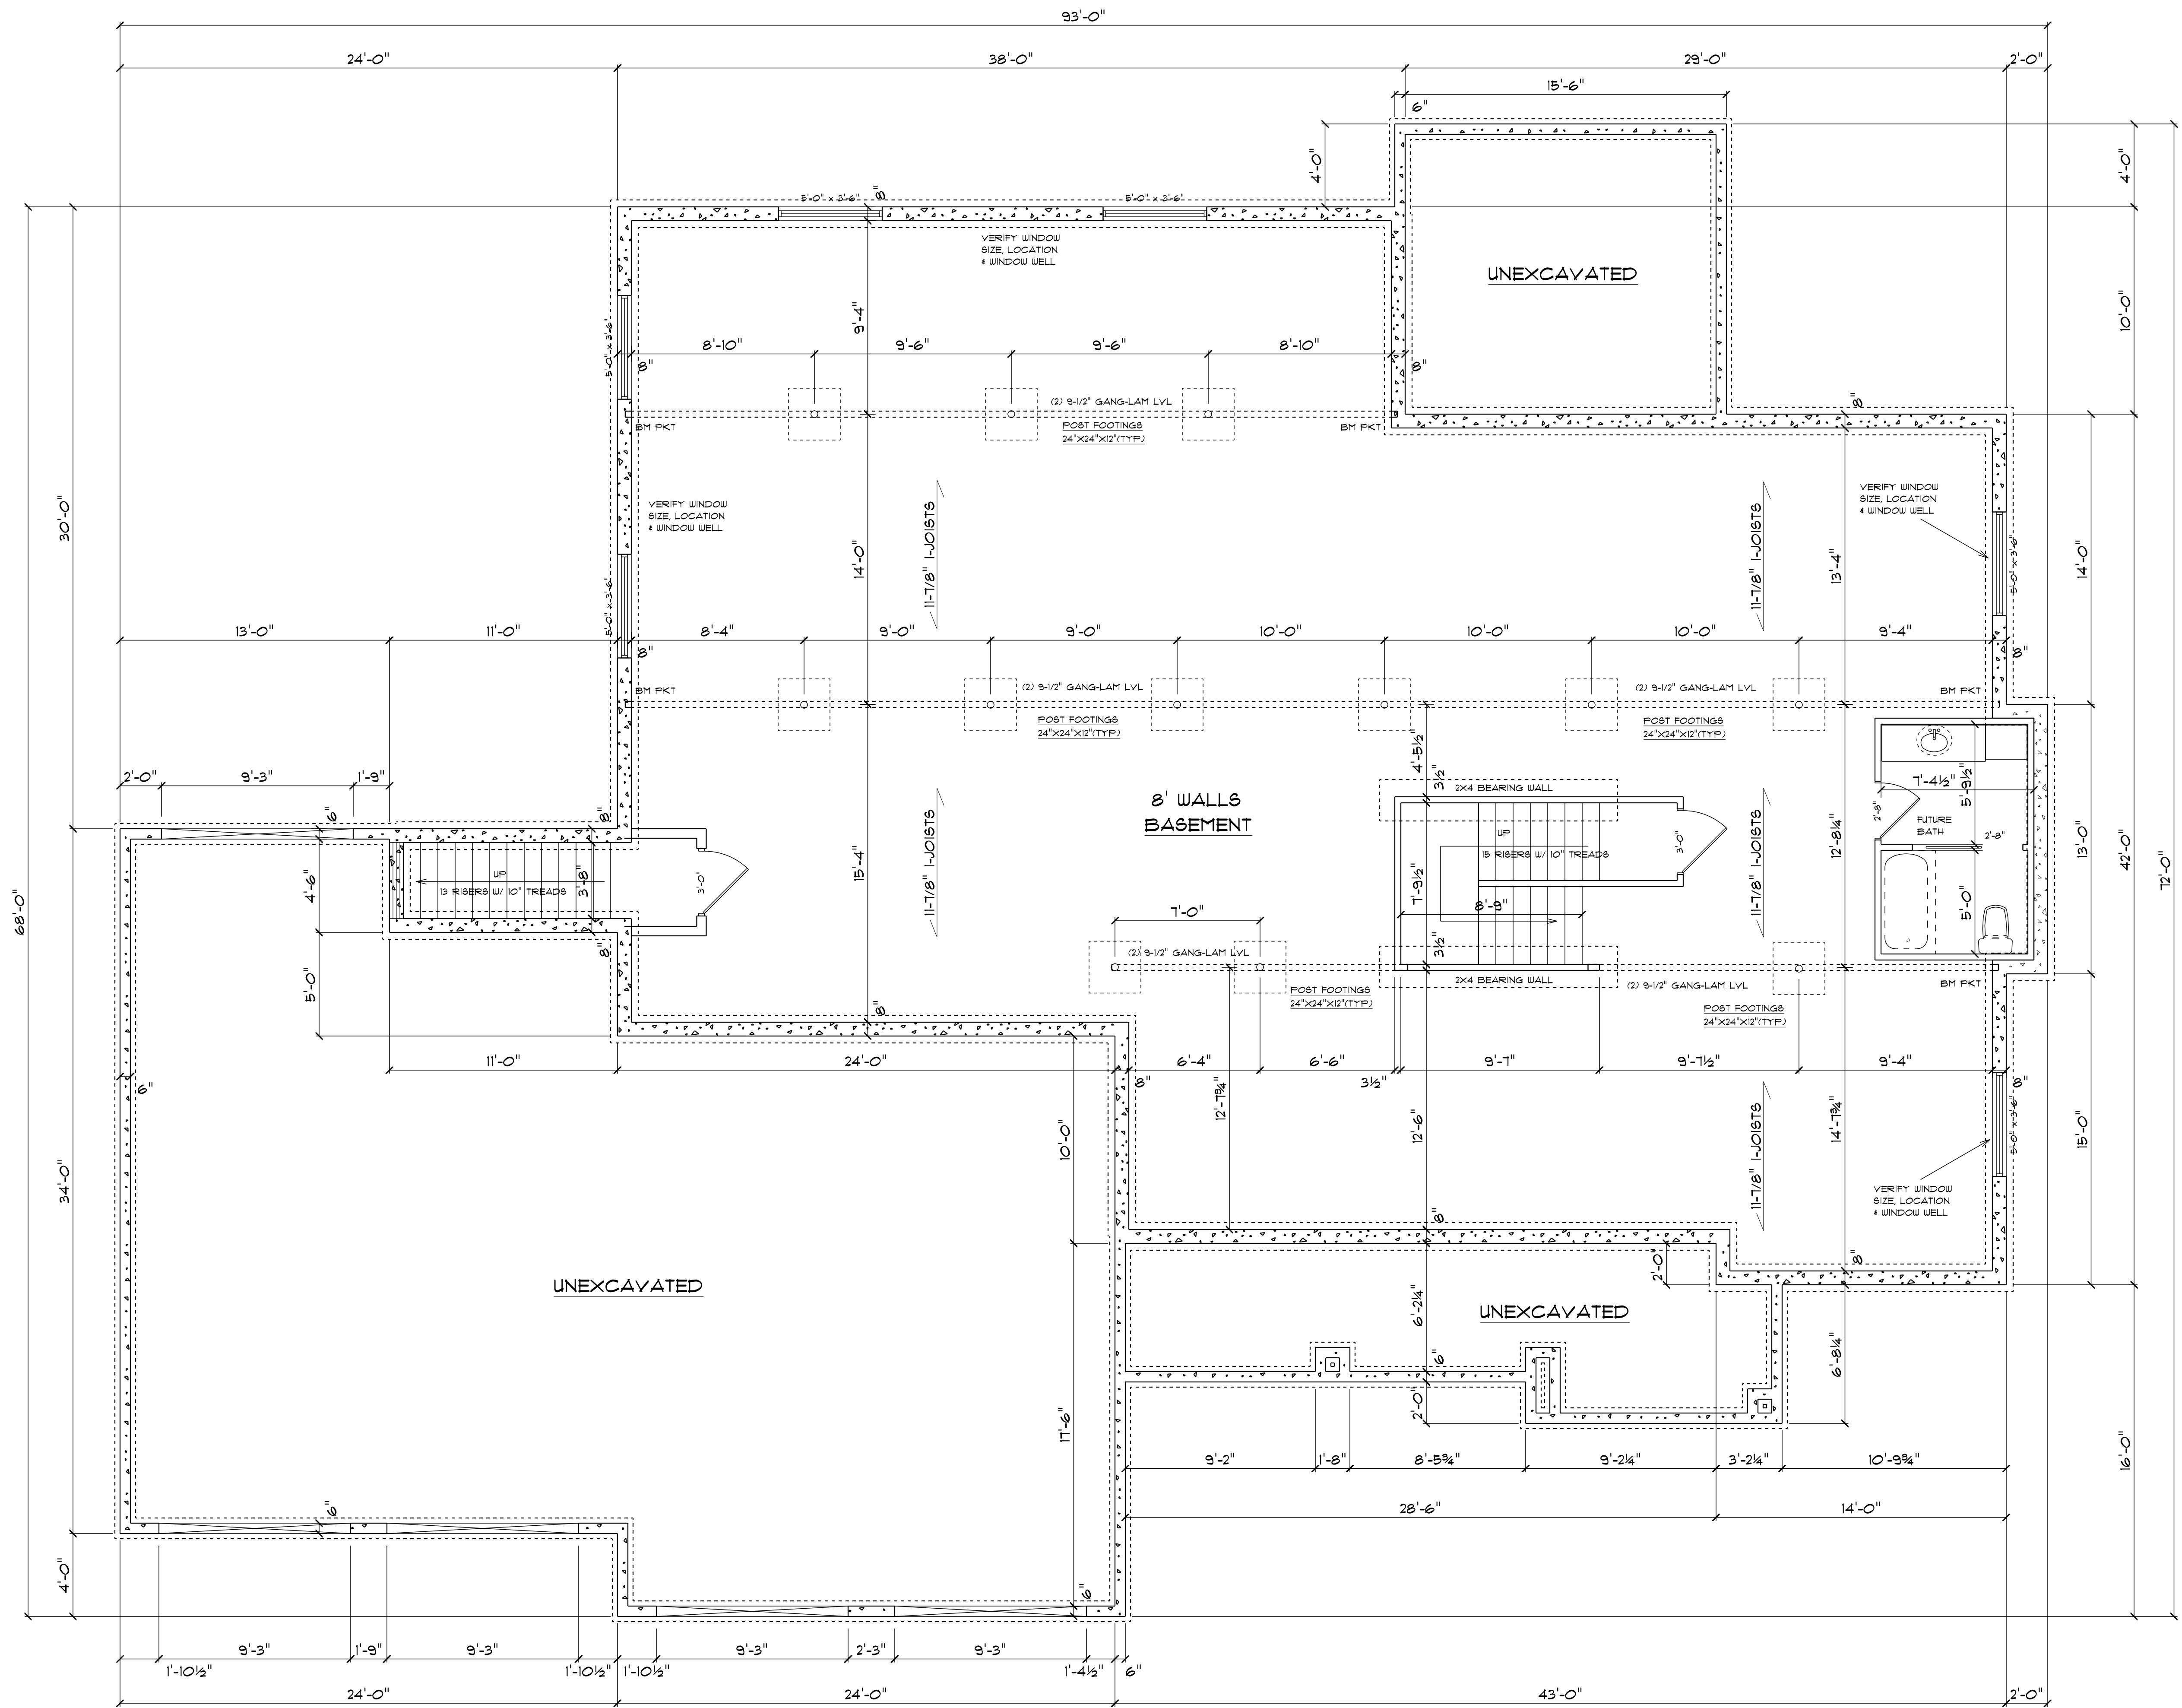

FOUNDATION PLAN


REVISION DATE:
9-22-2025

NEW RESIDENCE FOR:
THE LAUNDRIE FAMILY
WISCONSIN

DRAWN BY: M.P.
DATE: 9-15-2025
SCALE: 1/4"=1'-0"
DRAWING NO.

ALTHOUGH EVERY EFFORT
HAS BEEN MADE IN
PREPARING THESE PLANS
AND CHECKING THEM FOR
ACCURACY, THE
CONTRACTOR MUST CHECK
ALL DETAILS AND
DIMENSIONS AND BE
RESPONSIBLE FOR SAME.

SHEET NO.
3
OF
4

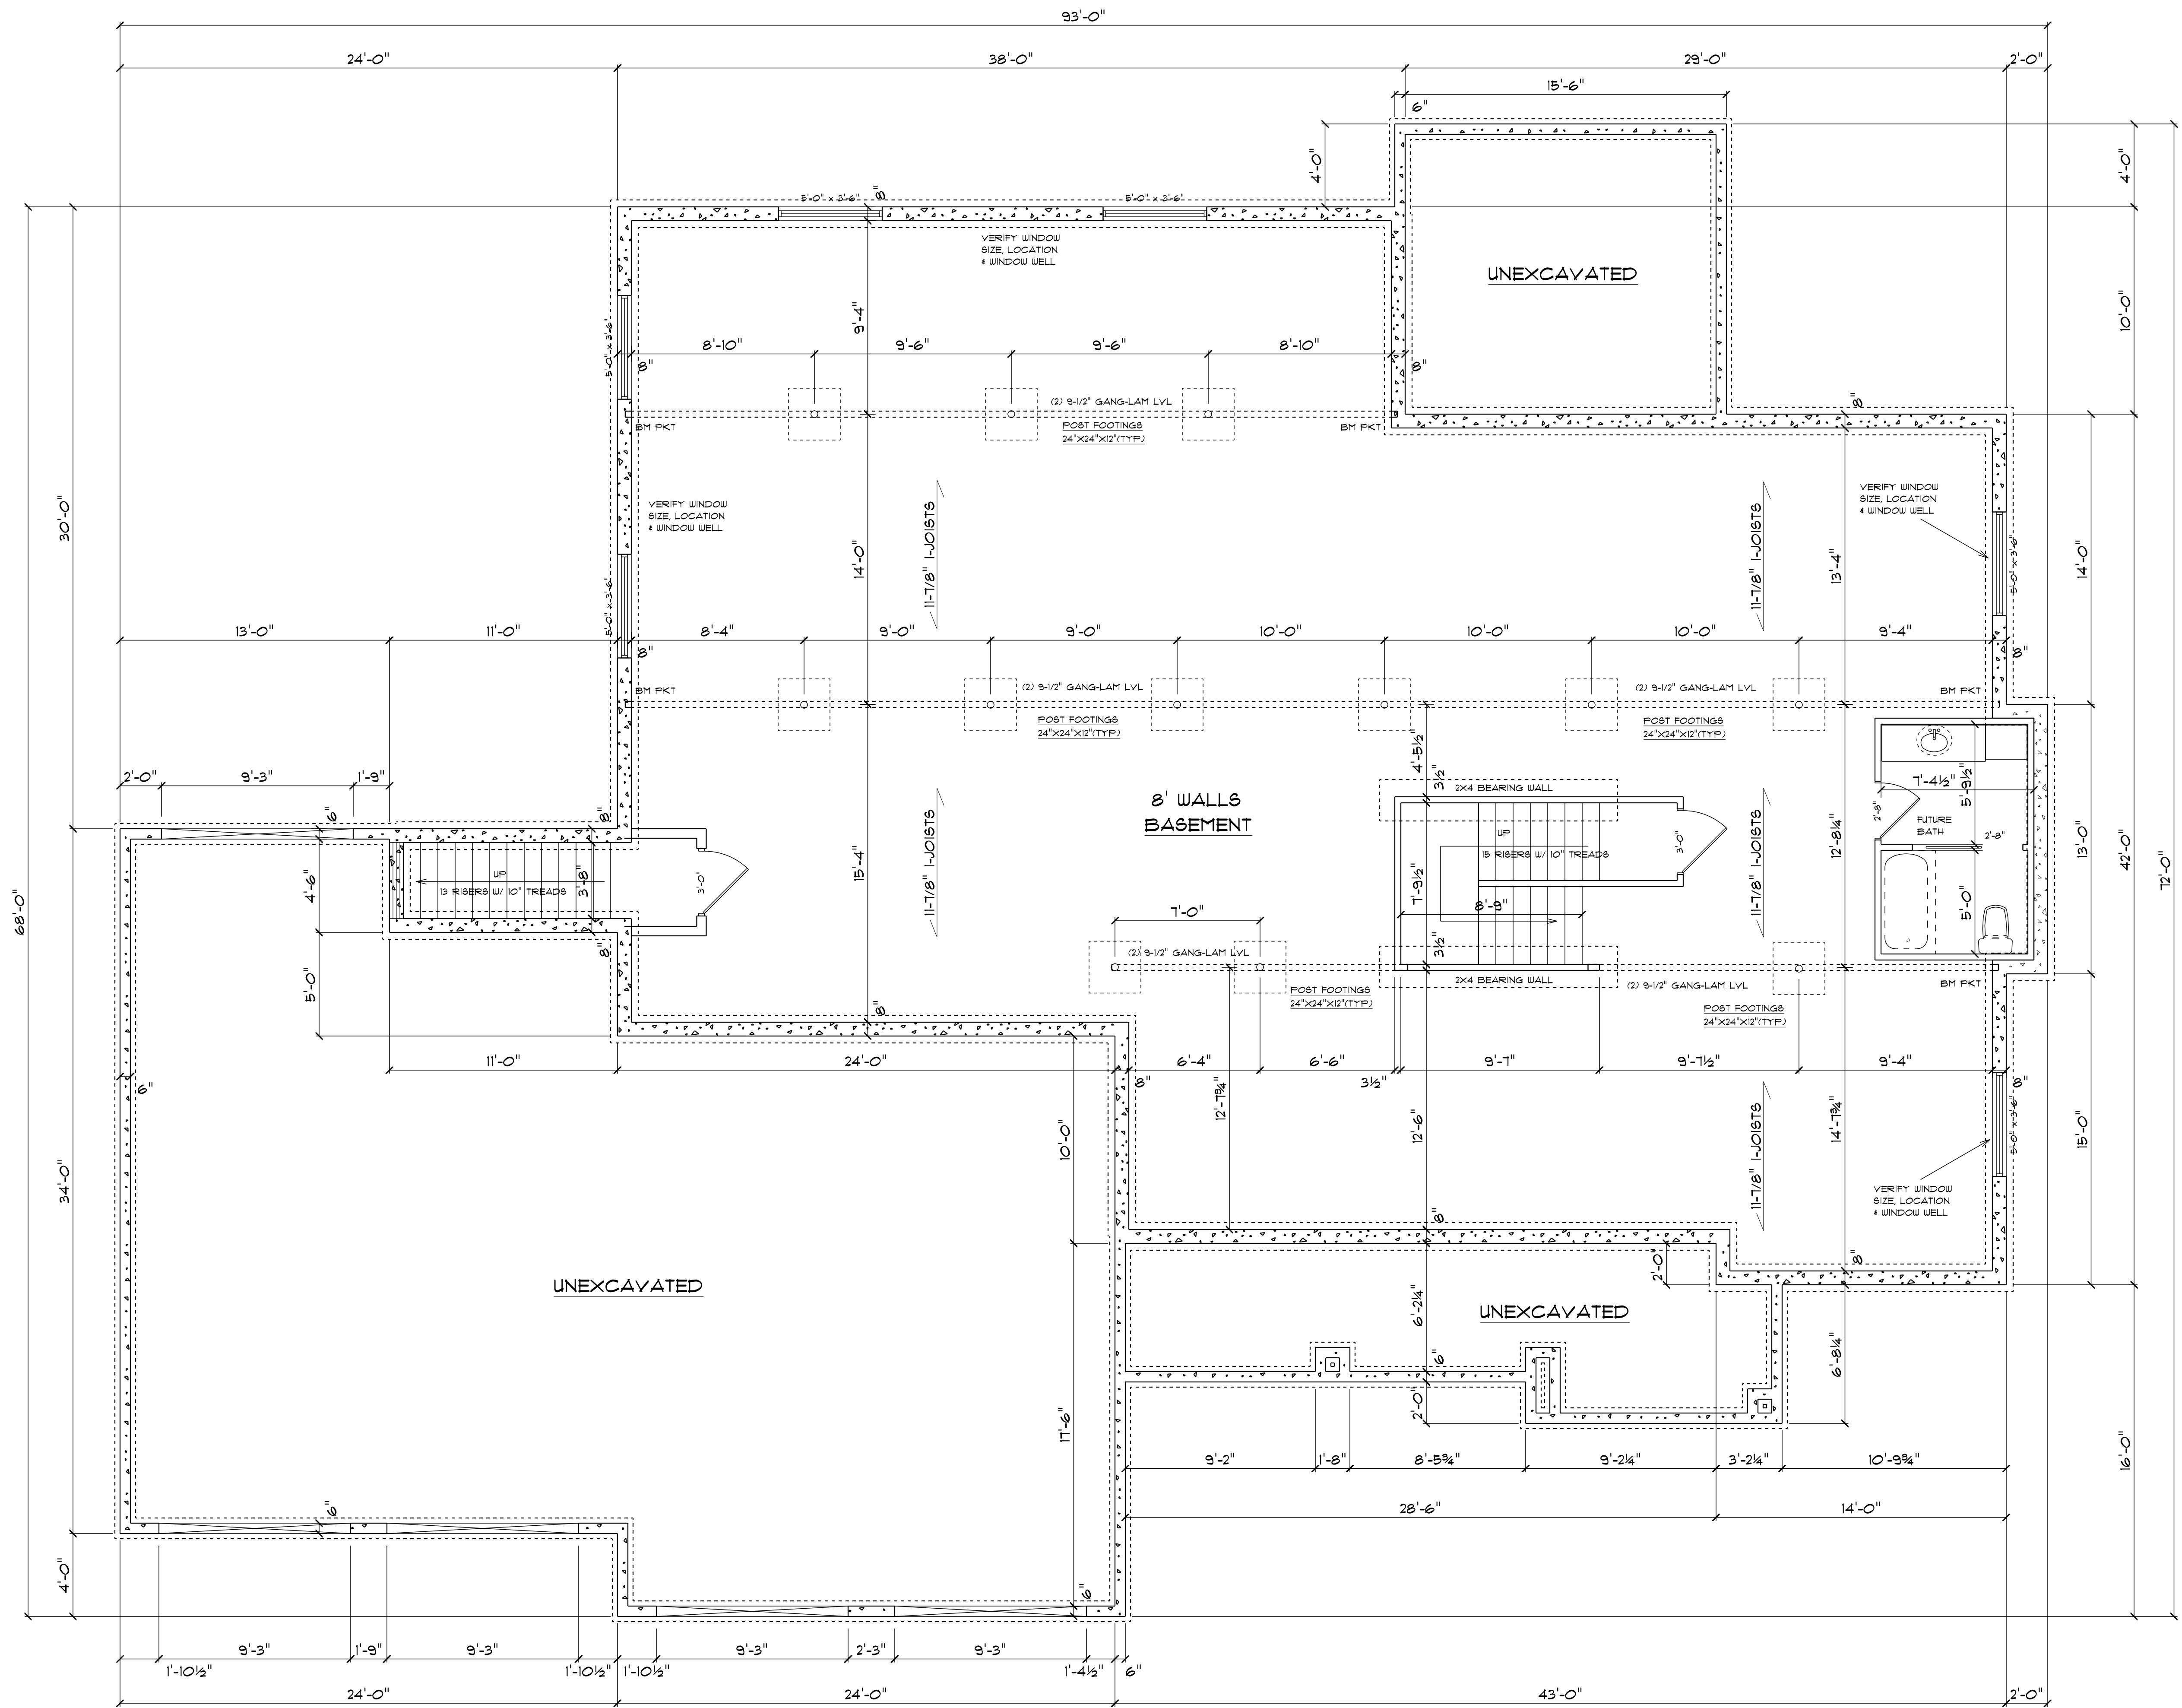

FOUNDATION PLAN


REVISION DATE:
9-22-2025

NEW RESIDENCE FOR:
THE LAUNDRIE FAMILY
WISCONSIN

DRAWN BY: M.P.
DATE: 9-15-2025
SCALE: 1/4"=1'-0"
DRAWING NO.

ALTHOUGH EVERY EFFORT
HAS BEEN MADE IN
PREPARING THESE PLANS
AND CHECKING THEM FOR
ACCURACY, THE
CONTRACTOR MUST CHECK
ALL DETAILS AND
DIMENSIONS AND BE
RESPONSIBLE FOR SAME.

SHEET NO.
3
OF
4

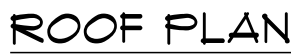

REVISION DATE:	
NEW RESIDENCE FOR: THE LAUNDRIE FAMILY NASCHEM, WISCONSIN	
DRAWN BY:	M.P.
DATE:	9-15-2025
SCALE:	1/4"=1'-0"
DRAWING NO.:	ALTHOUGH EVERY EFFORT HAS BEEN MADE IN PREPARING THESE PLANS AND CHECKING THEM FOR ACCURACY, THE CONTRACTOR MUST CHECK ALL DETAILS AND DIMENSIONS AND BE RESPONSIBLE FOR SAME.
SHEET NO.:	4 OF 4